


FAMILY HOUSE · SECTION · RIGHT ARM

Road left · sunset right · floors 93.35 / 92.47 / 91.46 · second floor 96.08 / 95.20

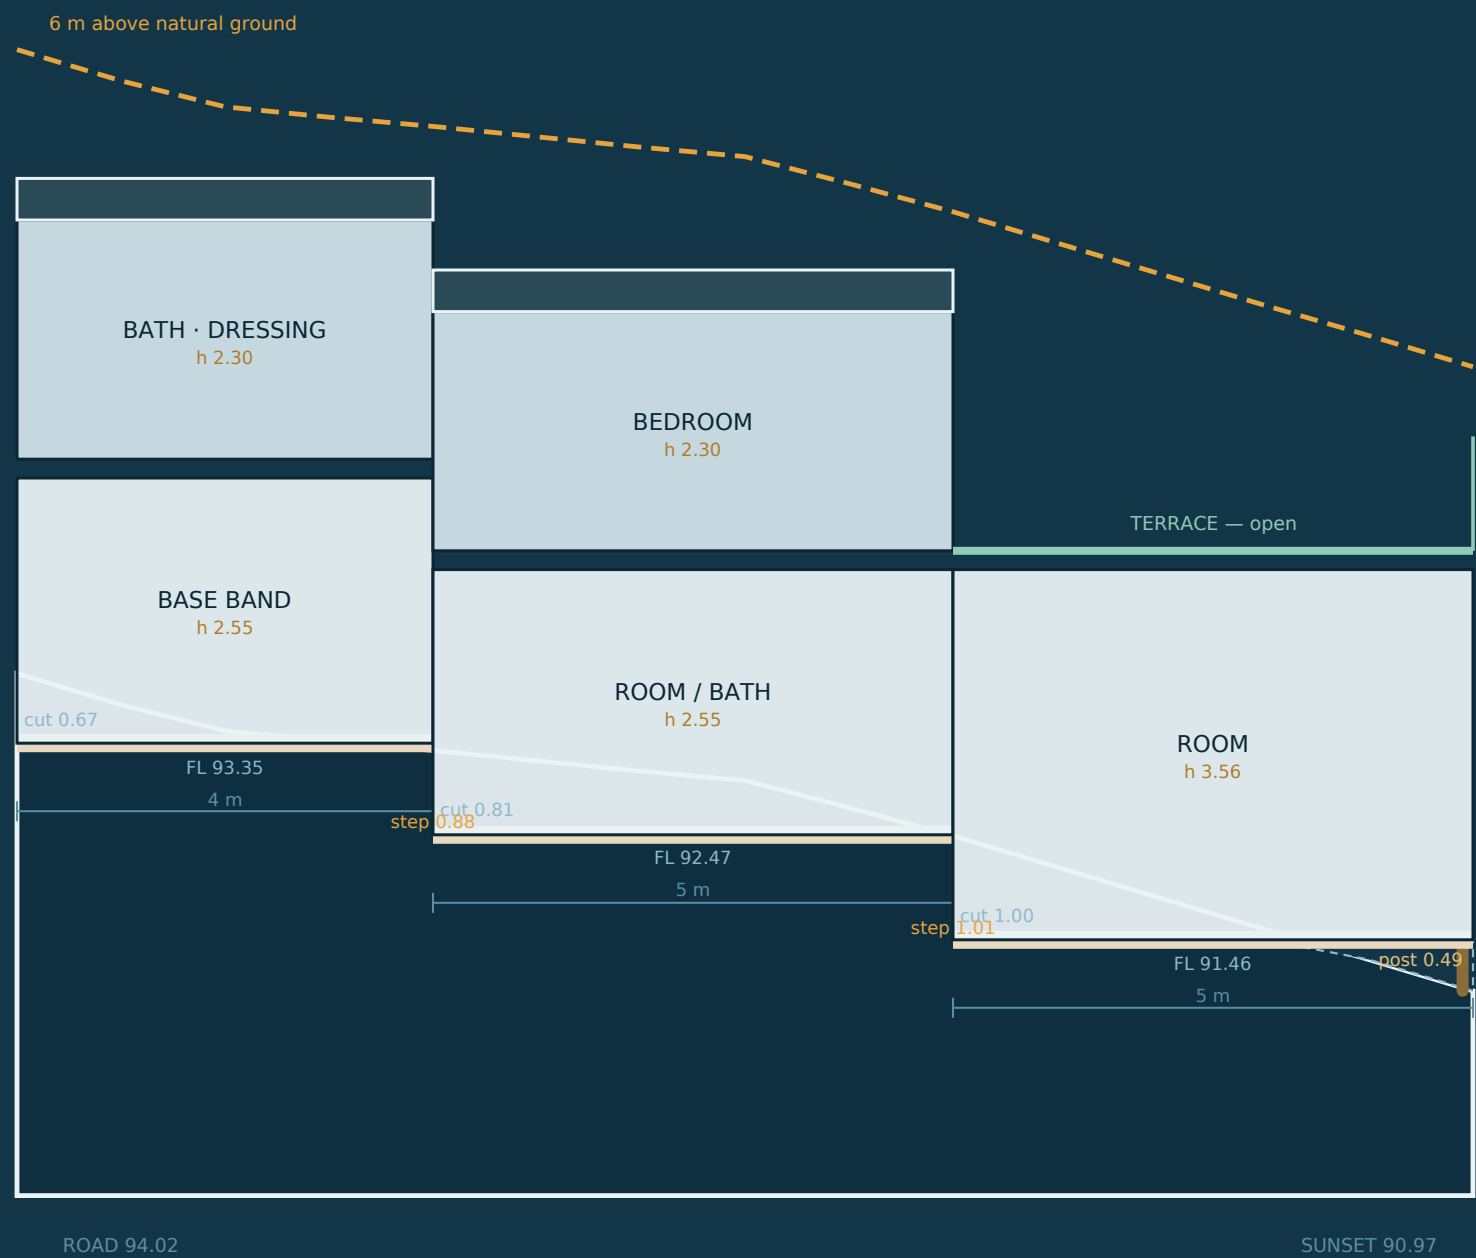

DASHED ORANGE — 6 m above natural ground

post — height of support below the slab

cut — excavation into the slope, max 1.00 m

h — clear ceiling height